


2 HARBORFRONT PARK

Miami, as a coastal city, is known for its close relationship with marine life and seafood.

Moreover, climate change is disrupting the local marine system and impacting the harvest of the fishery. The city is experiencing increase in the frequency and intensity of hurricanes/storms, impacting the livelihood of organisms.

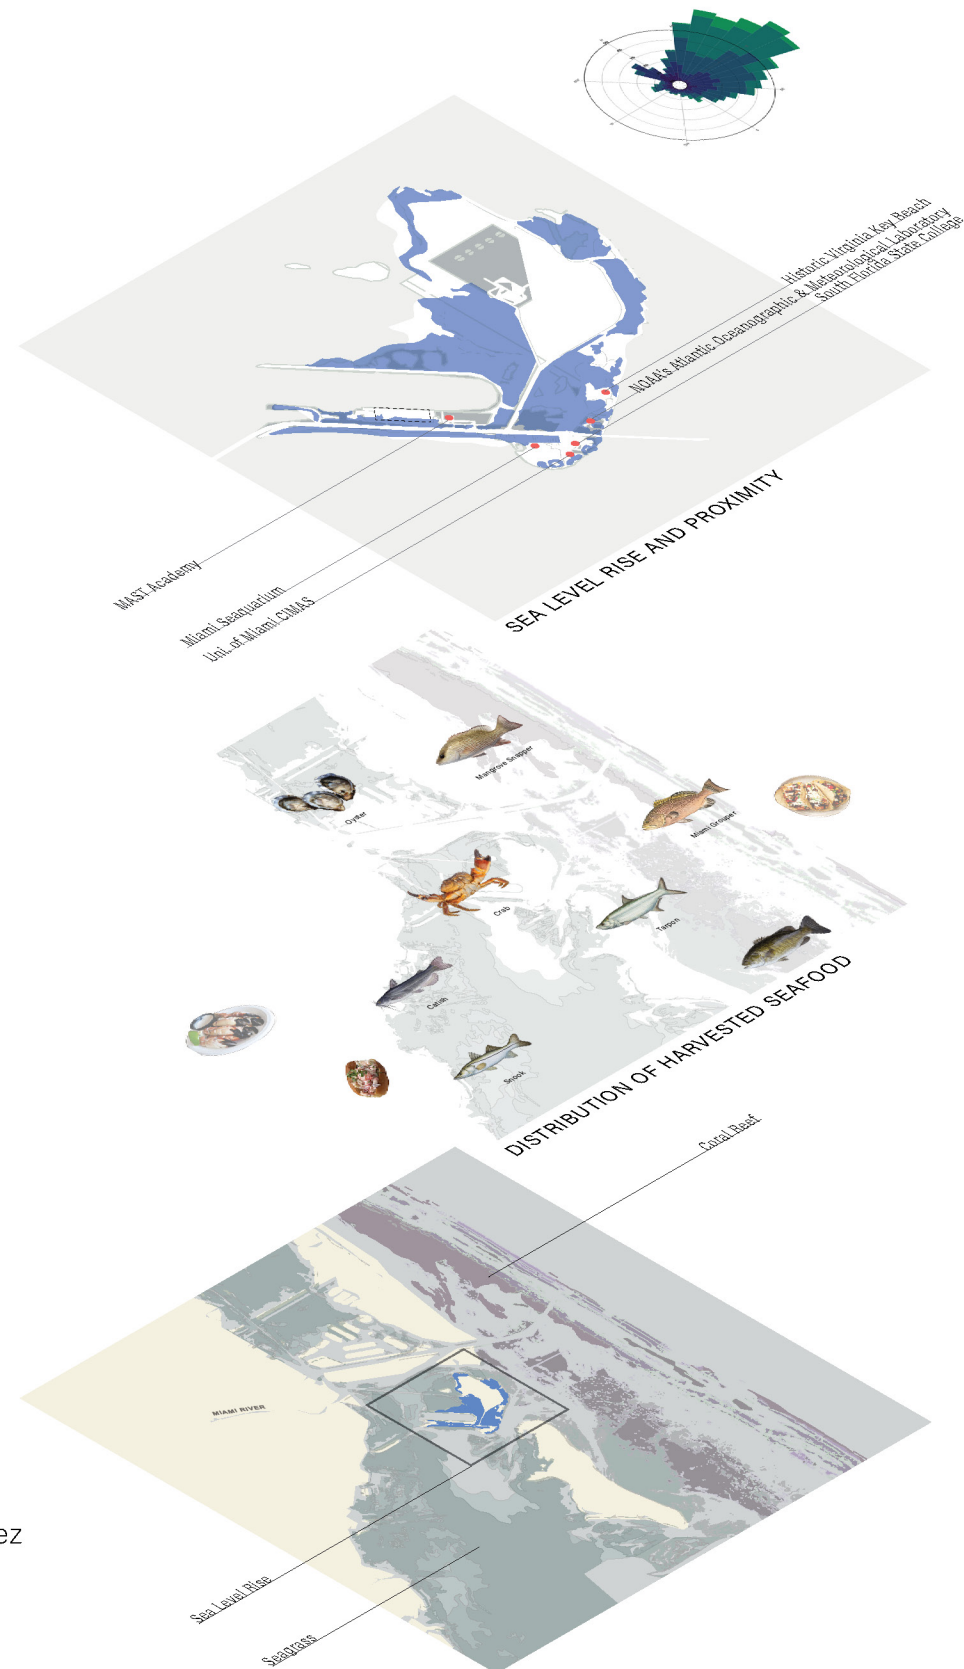

2023 Spring Studio




Pair-Partner Project: Victoria Lopez

Advisor: Traci Birch

Location: Miami, Florida

Duration: 2 Months

Softwares: Rhinoceros, ClimateStudio, ArcGIS, Lumion, Google Earth Pro, Adobe Suite (Photoshop, Illustrator, Indesign)

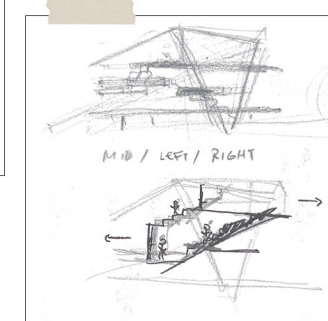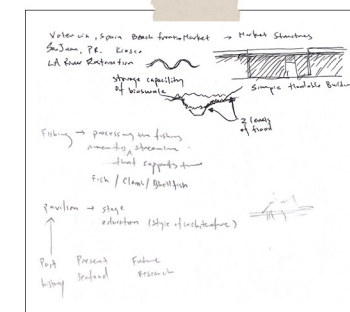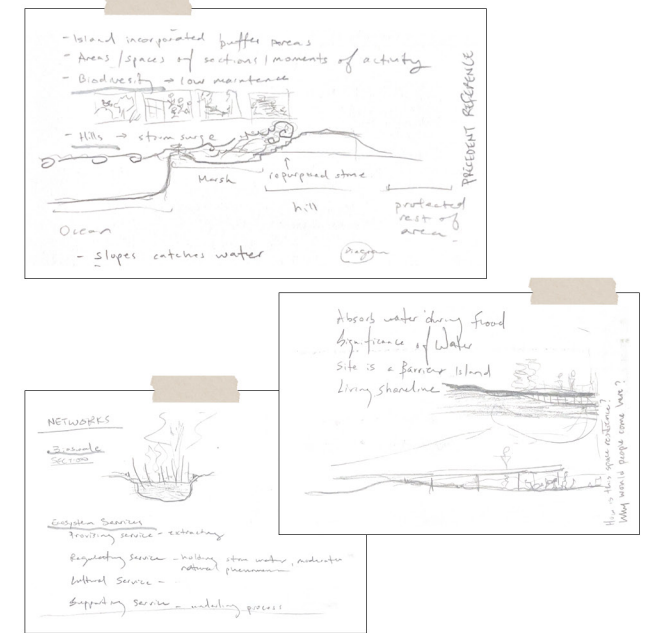


		Problems	Needs	Facts	Goals	Concepts
FORM	Site	Storm surge flood risk, sea level rise	public amenities, stadium renovation	city-owned	sea level rise protection, sustainable landscaping, attraction	reimagine a space able to withstand strong winds, not look at sea level rise threat but as a source for its new water management landscape
	Environment	consequences of climate change including sea level rise and impacts to infrastructure, ocean acidification and its impact to marine animals	sea level rise protection to the site and mainland	spacious site, next to the water, some vegetation, city of Miami view, retention ponds	playing with the landscape for sea level rise and flood protection, incorporate a lot of vegetation	alternative view to sea level rise to integrate into the future coexisting landscape: more vegetated space
	Connections	The marine stadium has been abandoned for decades	Revitalization; public attention	Historic Virginia Key park, NOAA and other nearby educational facilities	create partnerships with educational programs/ facilities to educate visitors on how the project works	educational spaces partnering with NOAA facilities, University of Miami research facility
FUNCTION	Individual	Sun exposures, currently limited utilization of the site	Provide thermal comfort and amenities that complements experience on site	Open space with many potential	Create a welcoming, comfortable, safe, public outdoor space for all	Imagine spaces that can hold a diverse range of activities and allow people to be in the same environment that is harmonious to nature
	Community	Community is losing connection with the site	opportunity for local merchants and recreation	cultural and historical reliance on water	cultural and historic education	The increase in amenities and activities will become attraction and reconnect the site with the community
	Activity	The original design of the space was only limited to boating	recreational spaces/amenities	Marine Stadium, close to the water	recreation and facilities areas	provide opportunity for educational space, research partnership, and day to day recreational activities
	Relationships	the site is in close relationship with water	increase productivity	opportunity for boating and fishing	provide a engaging and productive on-site experience	comfortable environment to attract and boost blue economy




Conceptual Design Collage
generated with Photoshop




Site Analysis
generated with Illustrator, Indesign

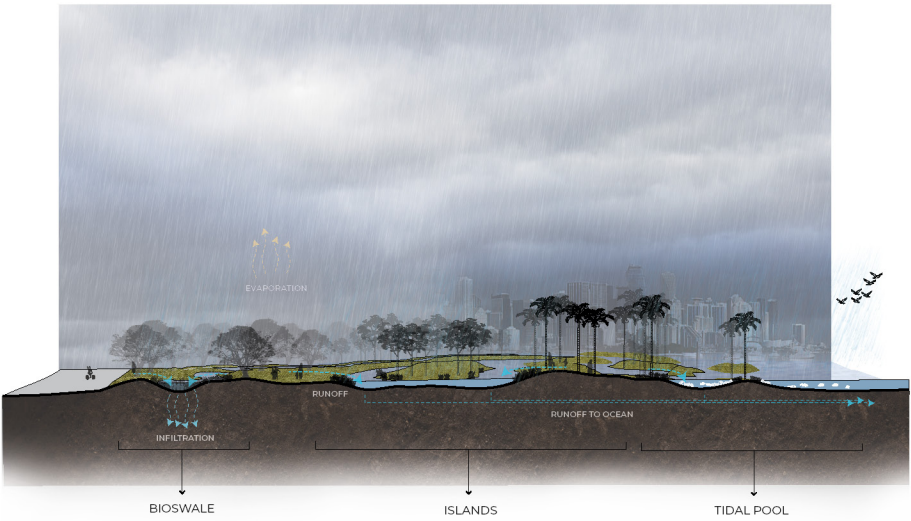

The landscape design focuses on constructing resilience against extreme weather and fostering biodiversities of small animals and juvenile fishes. It tackles various ecosystem services such as: bioswales, tidal pools and floodable spaces, and designated seafood extraction, processing activities, and markets on site.




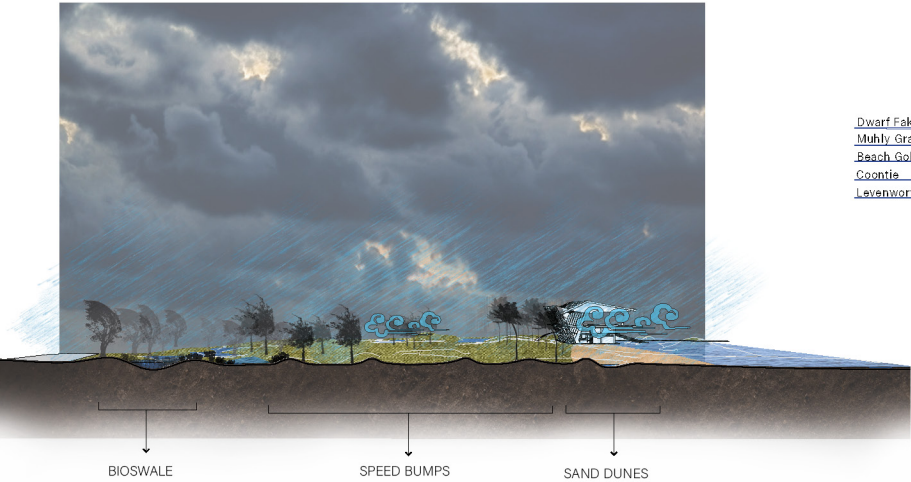



SECTION B generated with Illustrator

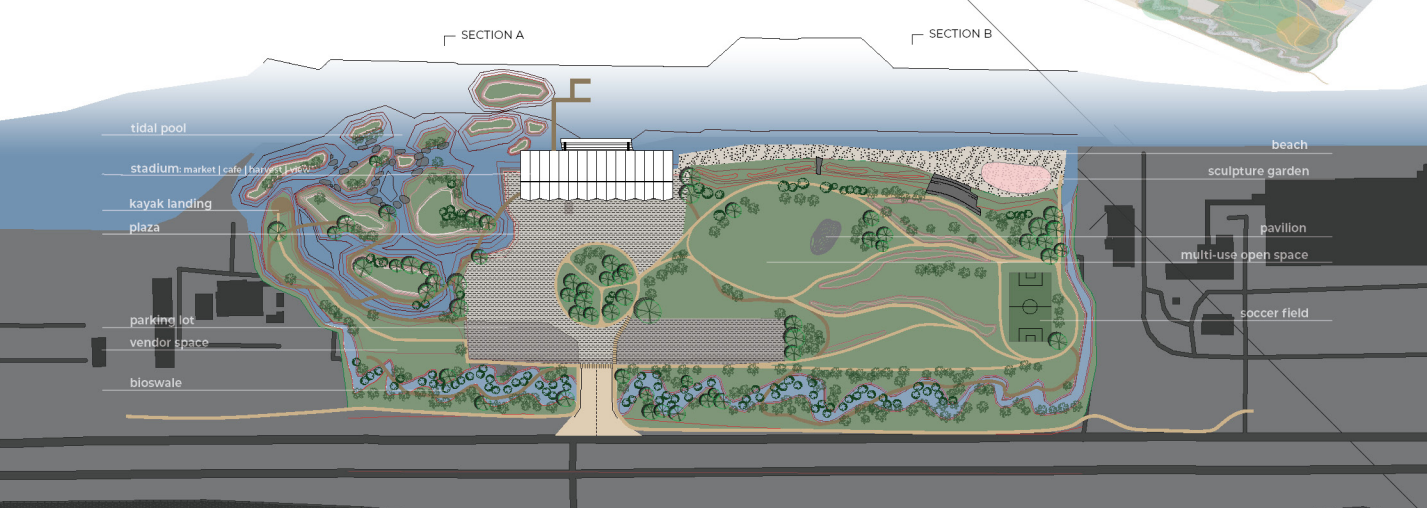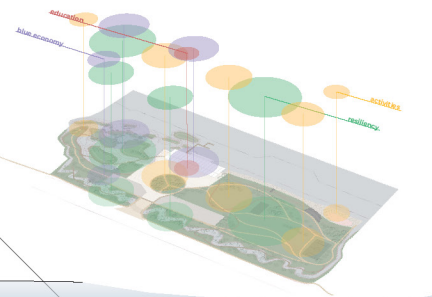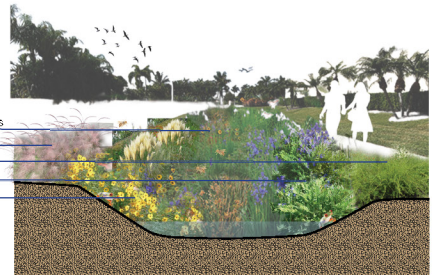

PROPOSED SITE PLAN generated with Illustrator

The building is designed to encourage natural air circulation and therefore, minimize reliance on mechanical energy systems. It houses seafood and local produce markets, a fishing/kayak deck and terrace seating facing the sea, and seafood restaurant. Overall, the building aims to support local vendors and seafood economy with existing regular market/park visitors and an ongoing tourist population.

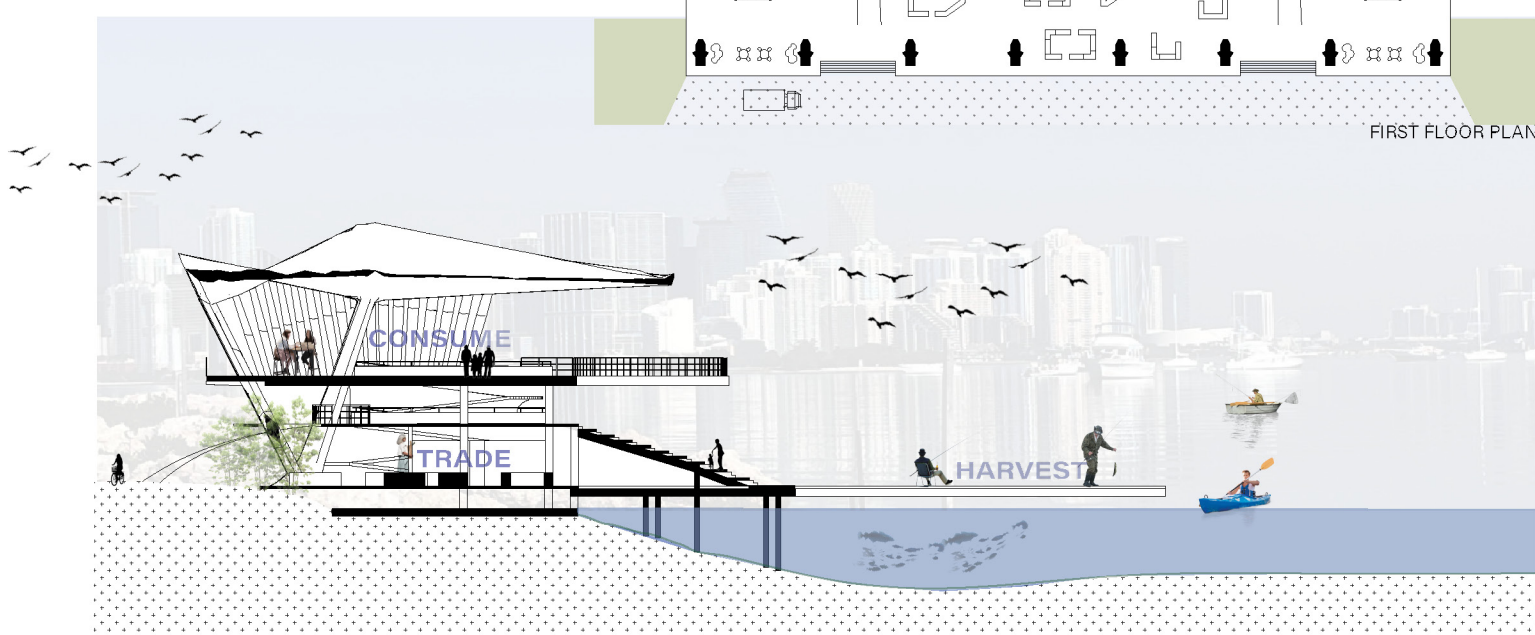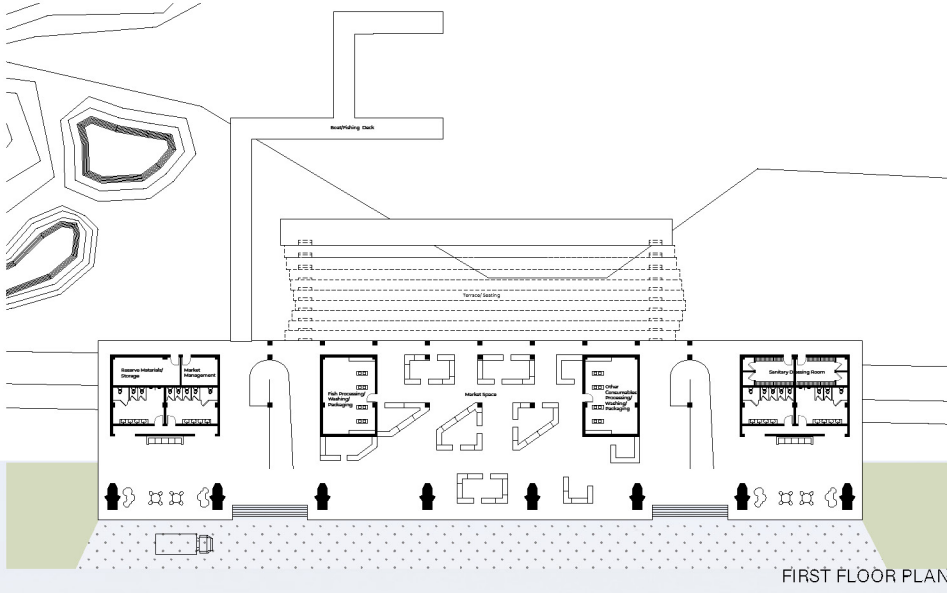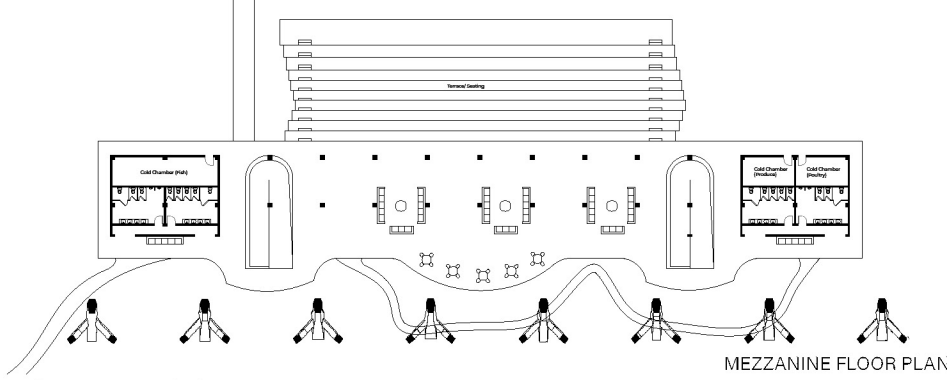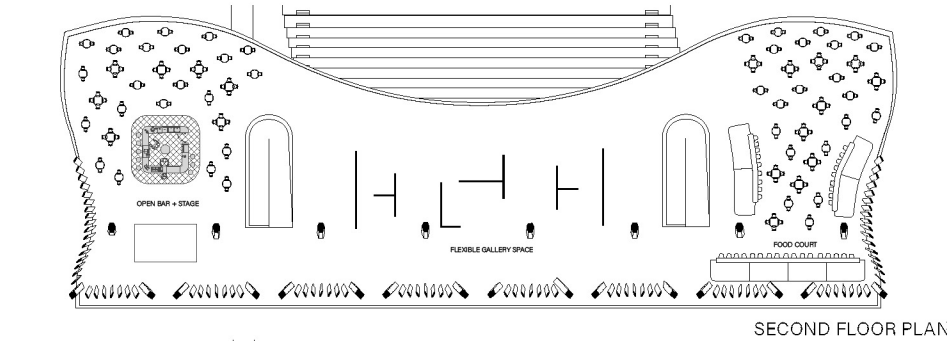

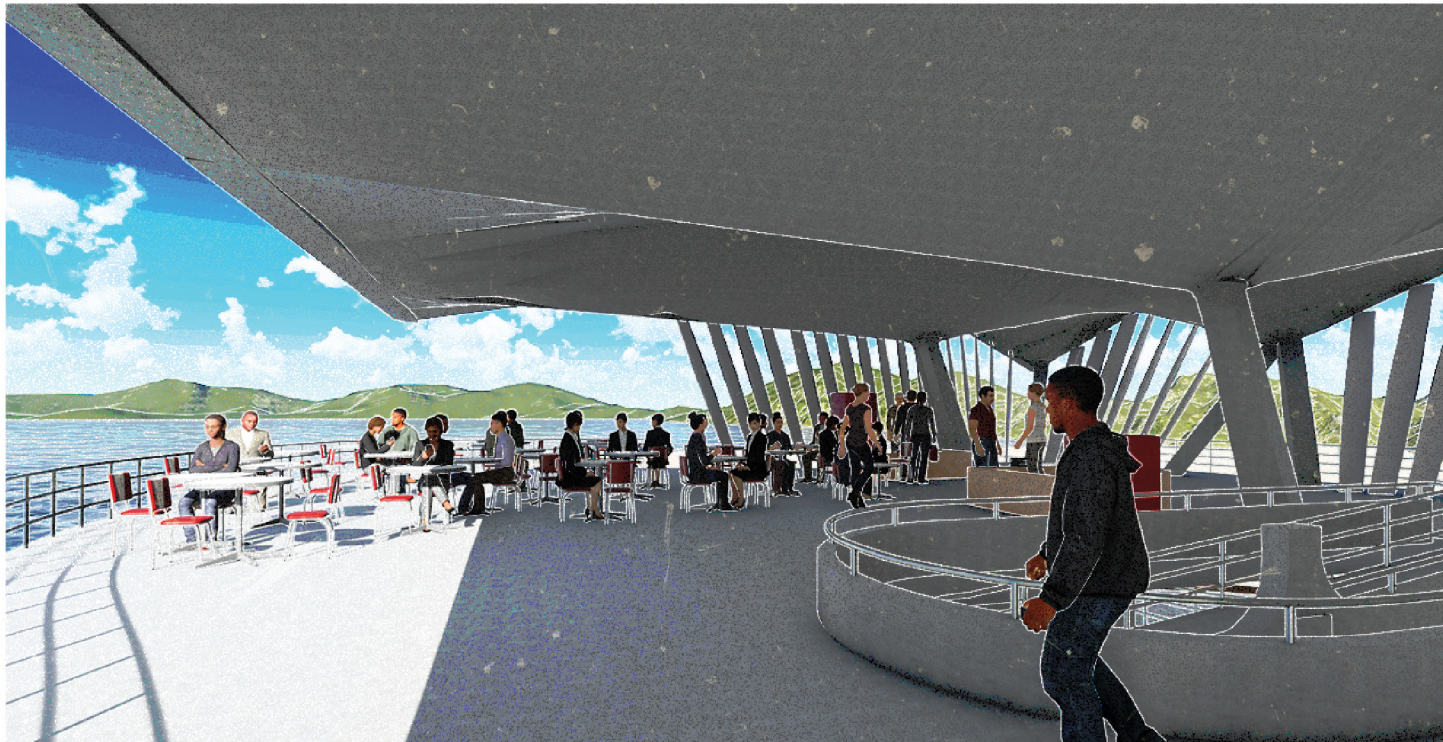



FOOD COURT ON SECOND FLOOR




HARVESTING DECK + TERRACING STEPS




FOOD MARKET ON FIRST FLOOR
generated with Lumion, Photoshop

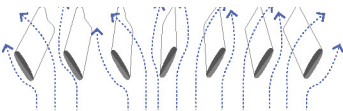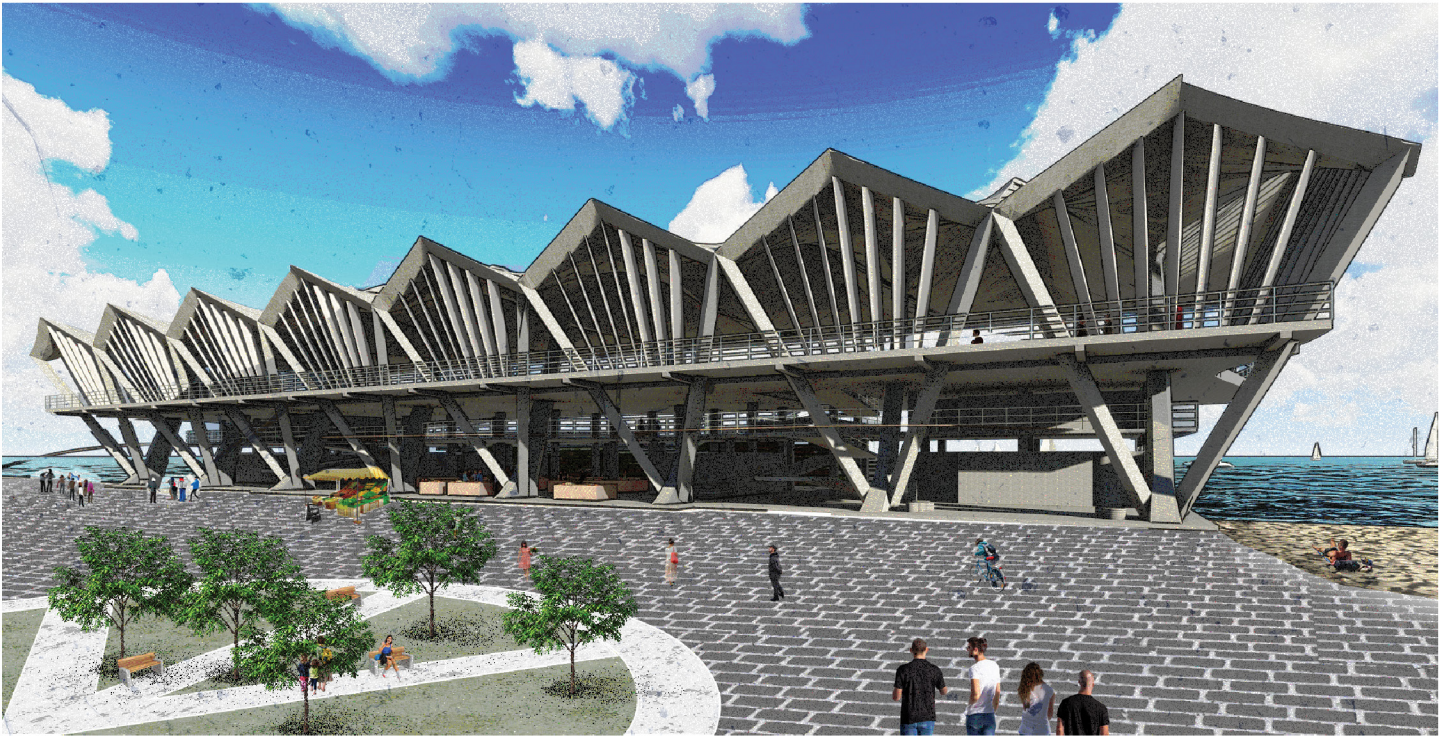


WIND FLOW ON FACADE

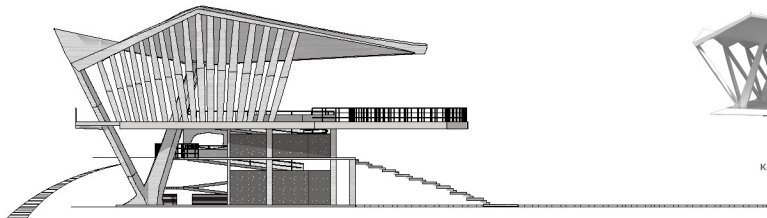

ELEVATION 1

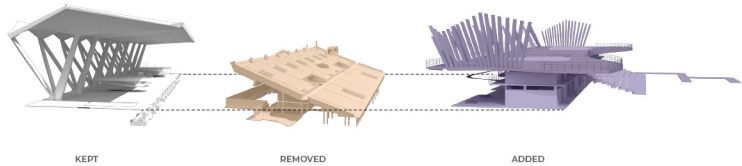

BUILDING MASS DIAGRAM

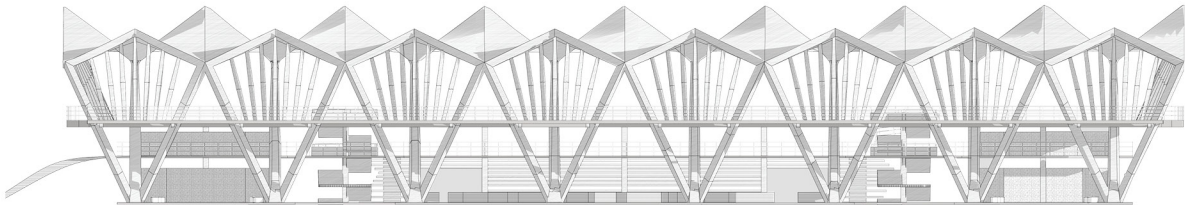

ELEVATION 2
generated with Rhinoceros3D